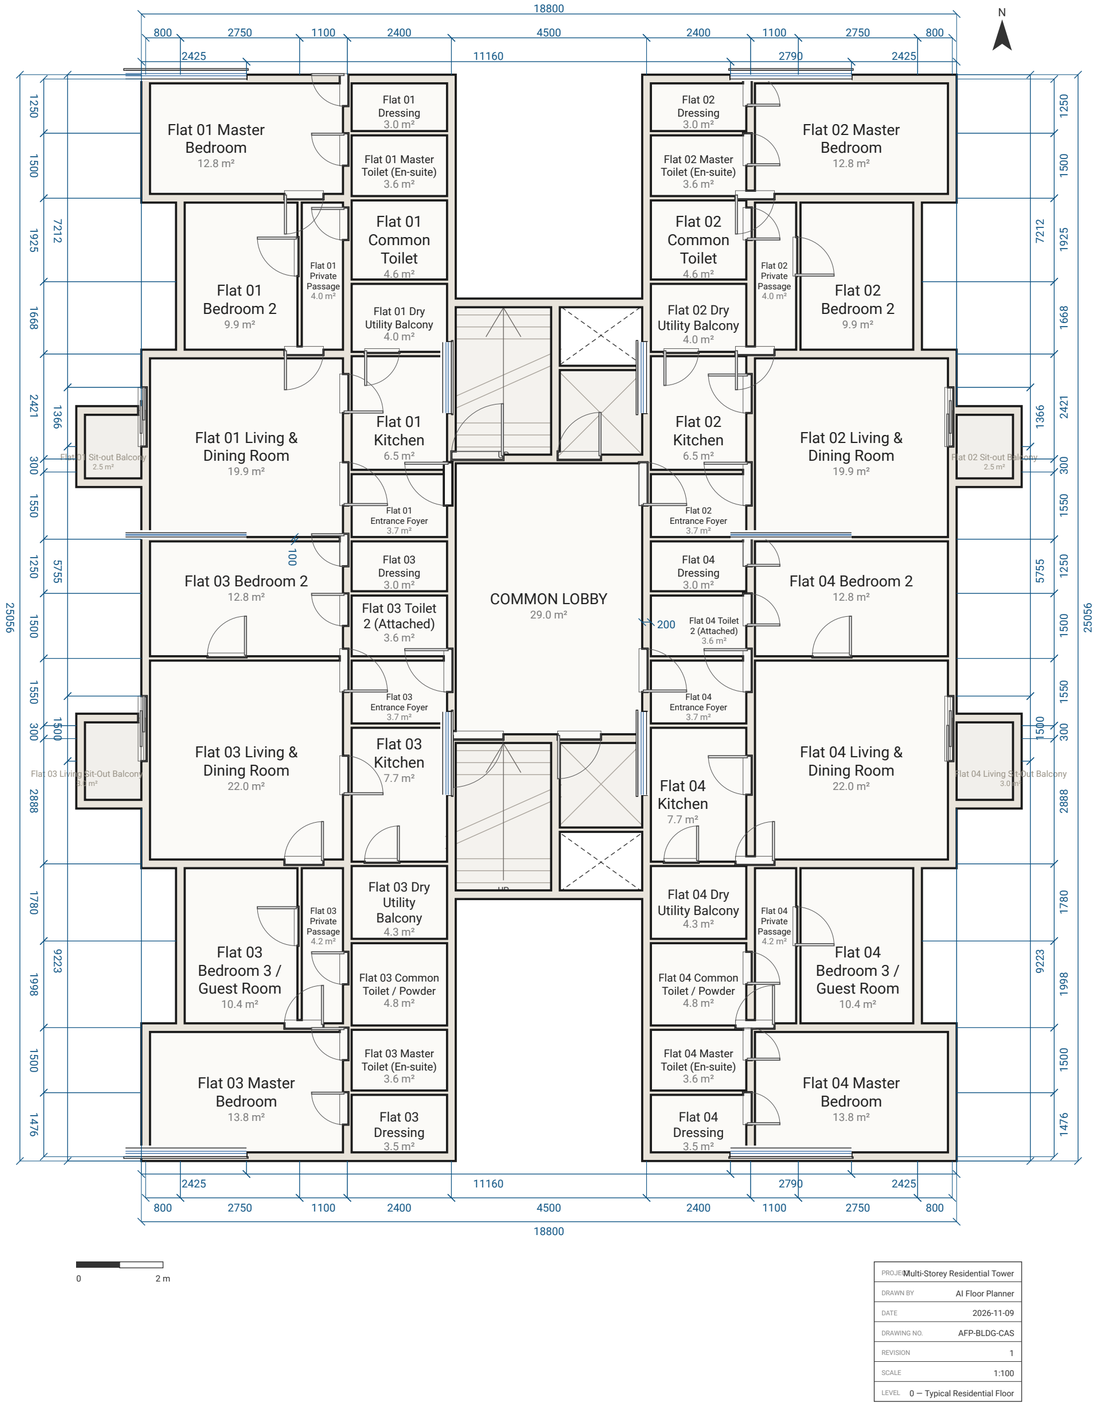

PROJECT	Multi-Storey Residential Tower
DRAWN BY	AI Floor Planner
DATE	2026-11-09
DRAWING NO.	AFP-BLDG-CAS
REVISION	1
SCALE	1:100
LEVEL	0 — Typical Residential Floor